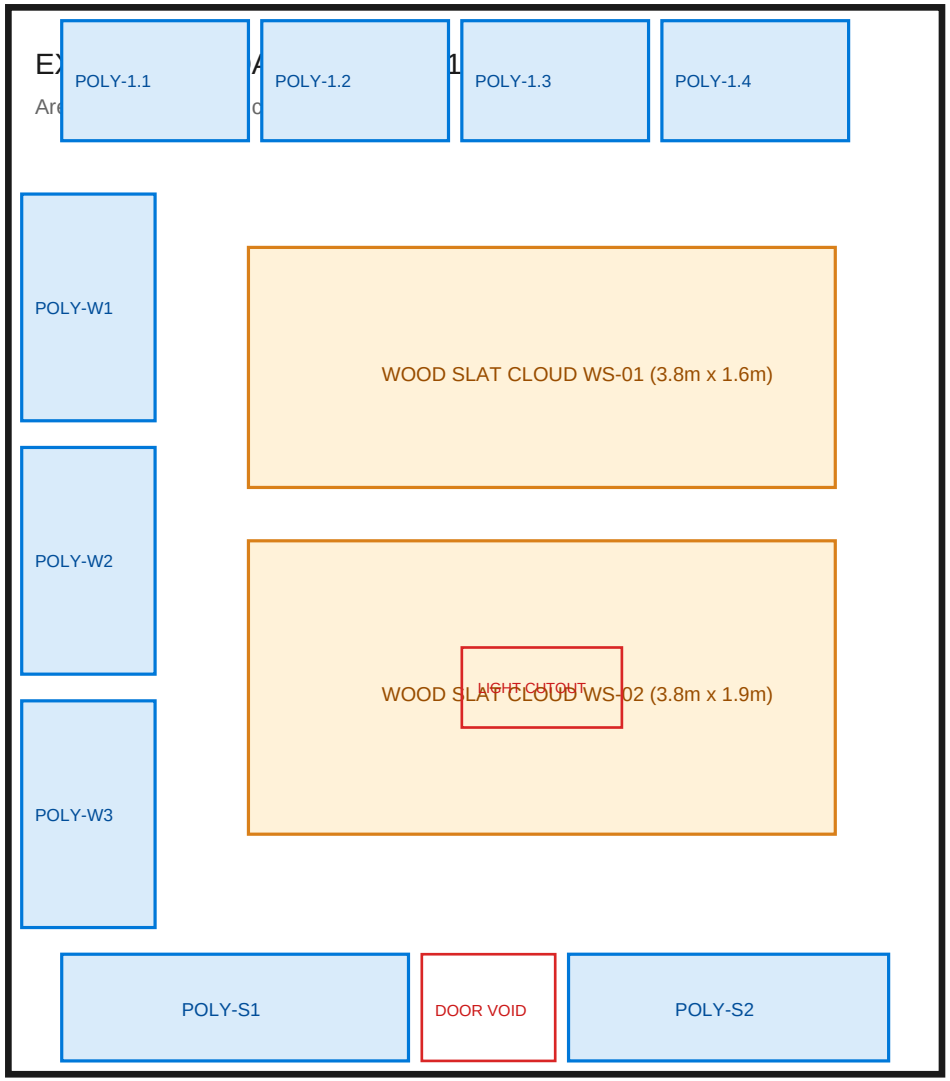

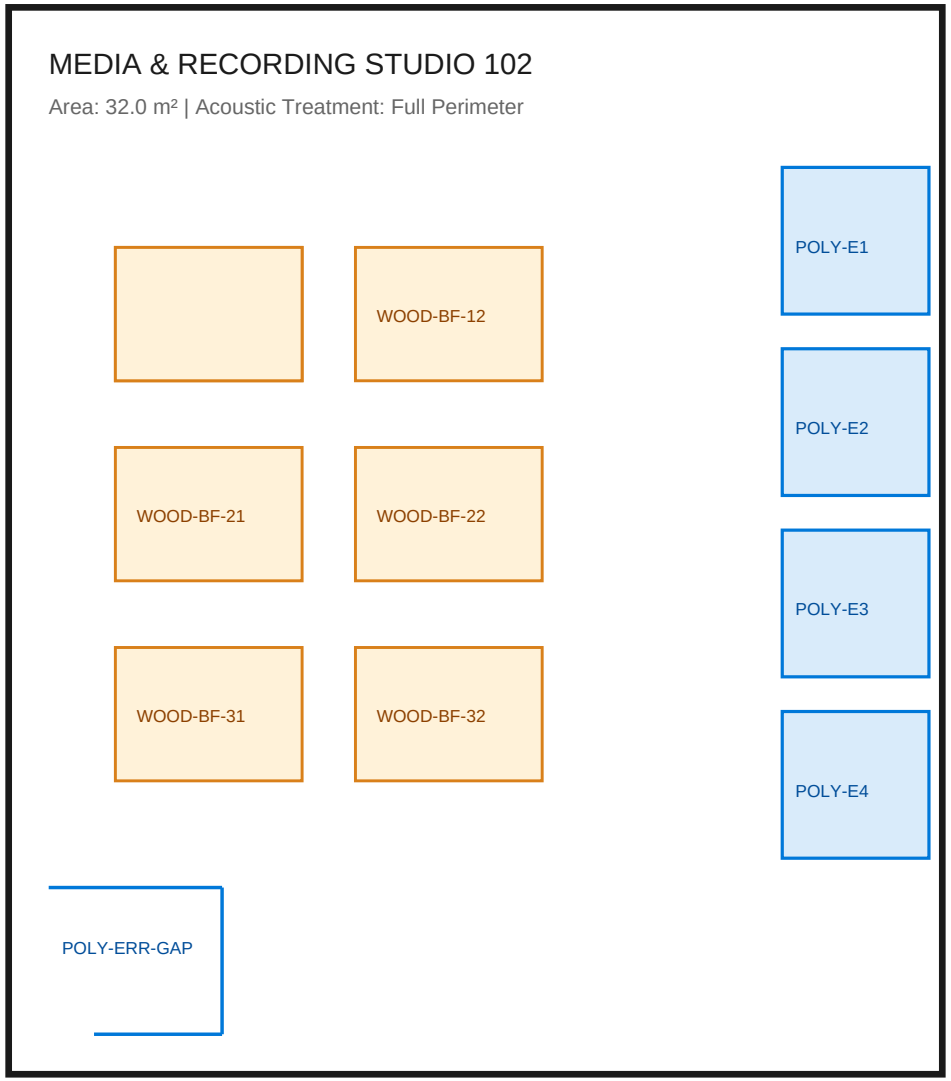

DETAIL CALLOUT SCALE: 1:100

LEGEND - ACOUSTIC SPECIFICATIONS

- Type AP-1: Polyester 9mm Acoustic Panel
- Type AC-2: Wood Slat Acoustic Ceiling Panel
- Wall Cutouts / Glazing Openings (Deductions)

GRAPHIC SCALE 1:50 (METERS)

0m 1m 2m 3m

PROJECT: ORION INNOVATION HUB

DRAWING: LEVEL 4 ACOUSTIC WALL & CEILING FITOUT

DWG NO: AC-401 | SHEET: 1 OF 3

SCALE: 1:50 | UNITS: MILLIMETERS

DATE: 2026-10-22 | DRAWN BY: QS/AEC TEAM

ORION INNOVATION HUB · ACOUSTIC FITOUT PACKAGE

GENERAL ARCHITECTURAL FITOUT SPECIFICATIONS & SCHEDULE OF FINISHES

1.0 GENERAL CONTRACT CONDITIONS:

1.1 All dimensions shall be verified on site by the trade contractor prior to shop fabrication.

1.2 Do not scale drawings. Architectural dimensions take precedence over CAD vector linework.

1.3 All acoustic panels to meet ASTM E84 Class A flame spread index and NRC >= 0.85 rating.

2.0 MATERIAL SPECIFICATIONS:

2.1 Polyester 9mm: 100% PET felt, minimum 60% post-consumer recycled fiber, density 1900 g/m².

2.2 Wood Slat Panel: Natural oak/walnut veneer on 9mm black acoustic polyester felt backing.

2.3 Fabric Wrapped 25mm: High-density 96 kg/m³ resin bonded fiberglass core with acoustically transparent textile.

3.0 FABRICATION, TOLERANCE & CUTTING:

3.1 Standard panel stock sizes: 2400 x 1200 mm and 2440 x 1220 mm.

3.2 Cutting kerf allowance: 3.0 mm for CNC router / panel saw blades.

3.3 Perimeter shadow gap joint allowance: 5.0 mm unless noted otherwise on architectural detail drawings.

NOTICE TO ESTIMATOR: THIS PAGE CONTAINS TEXT SPECIFICATIONS ONLY (NO ACOUSTIC TAKEOFF VECTOR POLYLINES).

PROJECT: ORION INNOVATION HUB

DRAWING: GENERAL NOTES & COVER SPECIFICATIONS

DWG NO: AC-001 | SHEET: 2 OF 3

SCALE: N.T.S. | UNITS: MILLIMETERS

DATE: 2026-10-22 | DRAWN BY: QS/AEC TEAM

AUDITORIUM & MULTIPURPOSE HALL 201

Seating Capacity: 180 Persons | Target RT60: 0.65s | High Absorption & Diffusion Fitout

REAR ACOUSTIC WALL · POLYESTER 9MM PANELS

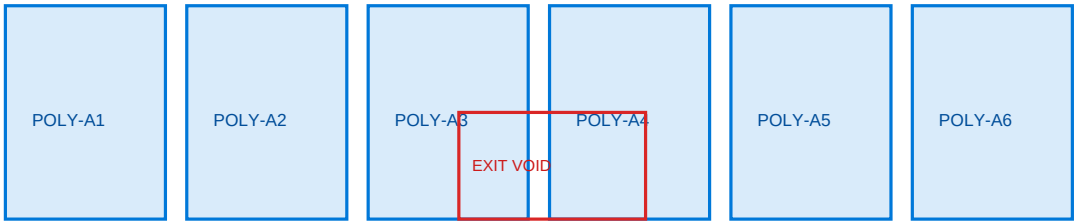

SIDE REFLECTOR & DIFFUSER WALLS · WOOD SLAT PANELS

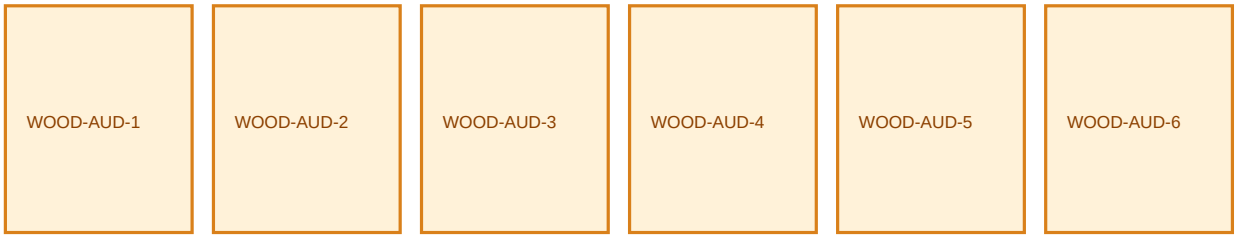

OVERHEAD CANOPY BAFFLES · FABRIC WRAPPED 25MM

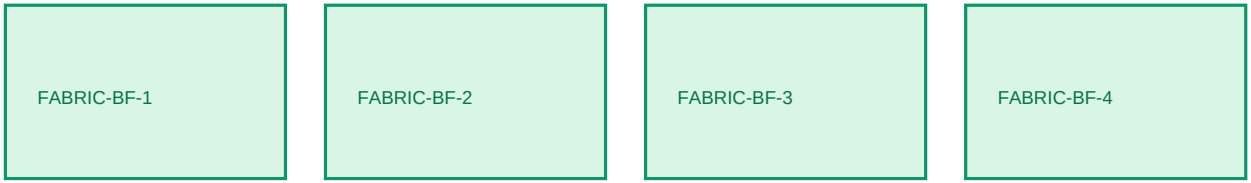

PROJECT: ORION INNOVATION HUB

DRAWING: LEVEL 5 AUDITORIUM ACOUSTIC TREATMENT

DWG NO: AC-501 | SHEET: 3 OF 3

SCALE: 1:50 | UNITS: MILLIMETERS

DATE: 2026-10-22 | DRAWN BY: QS/AEC TEAM